


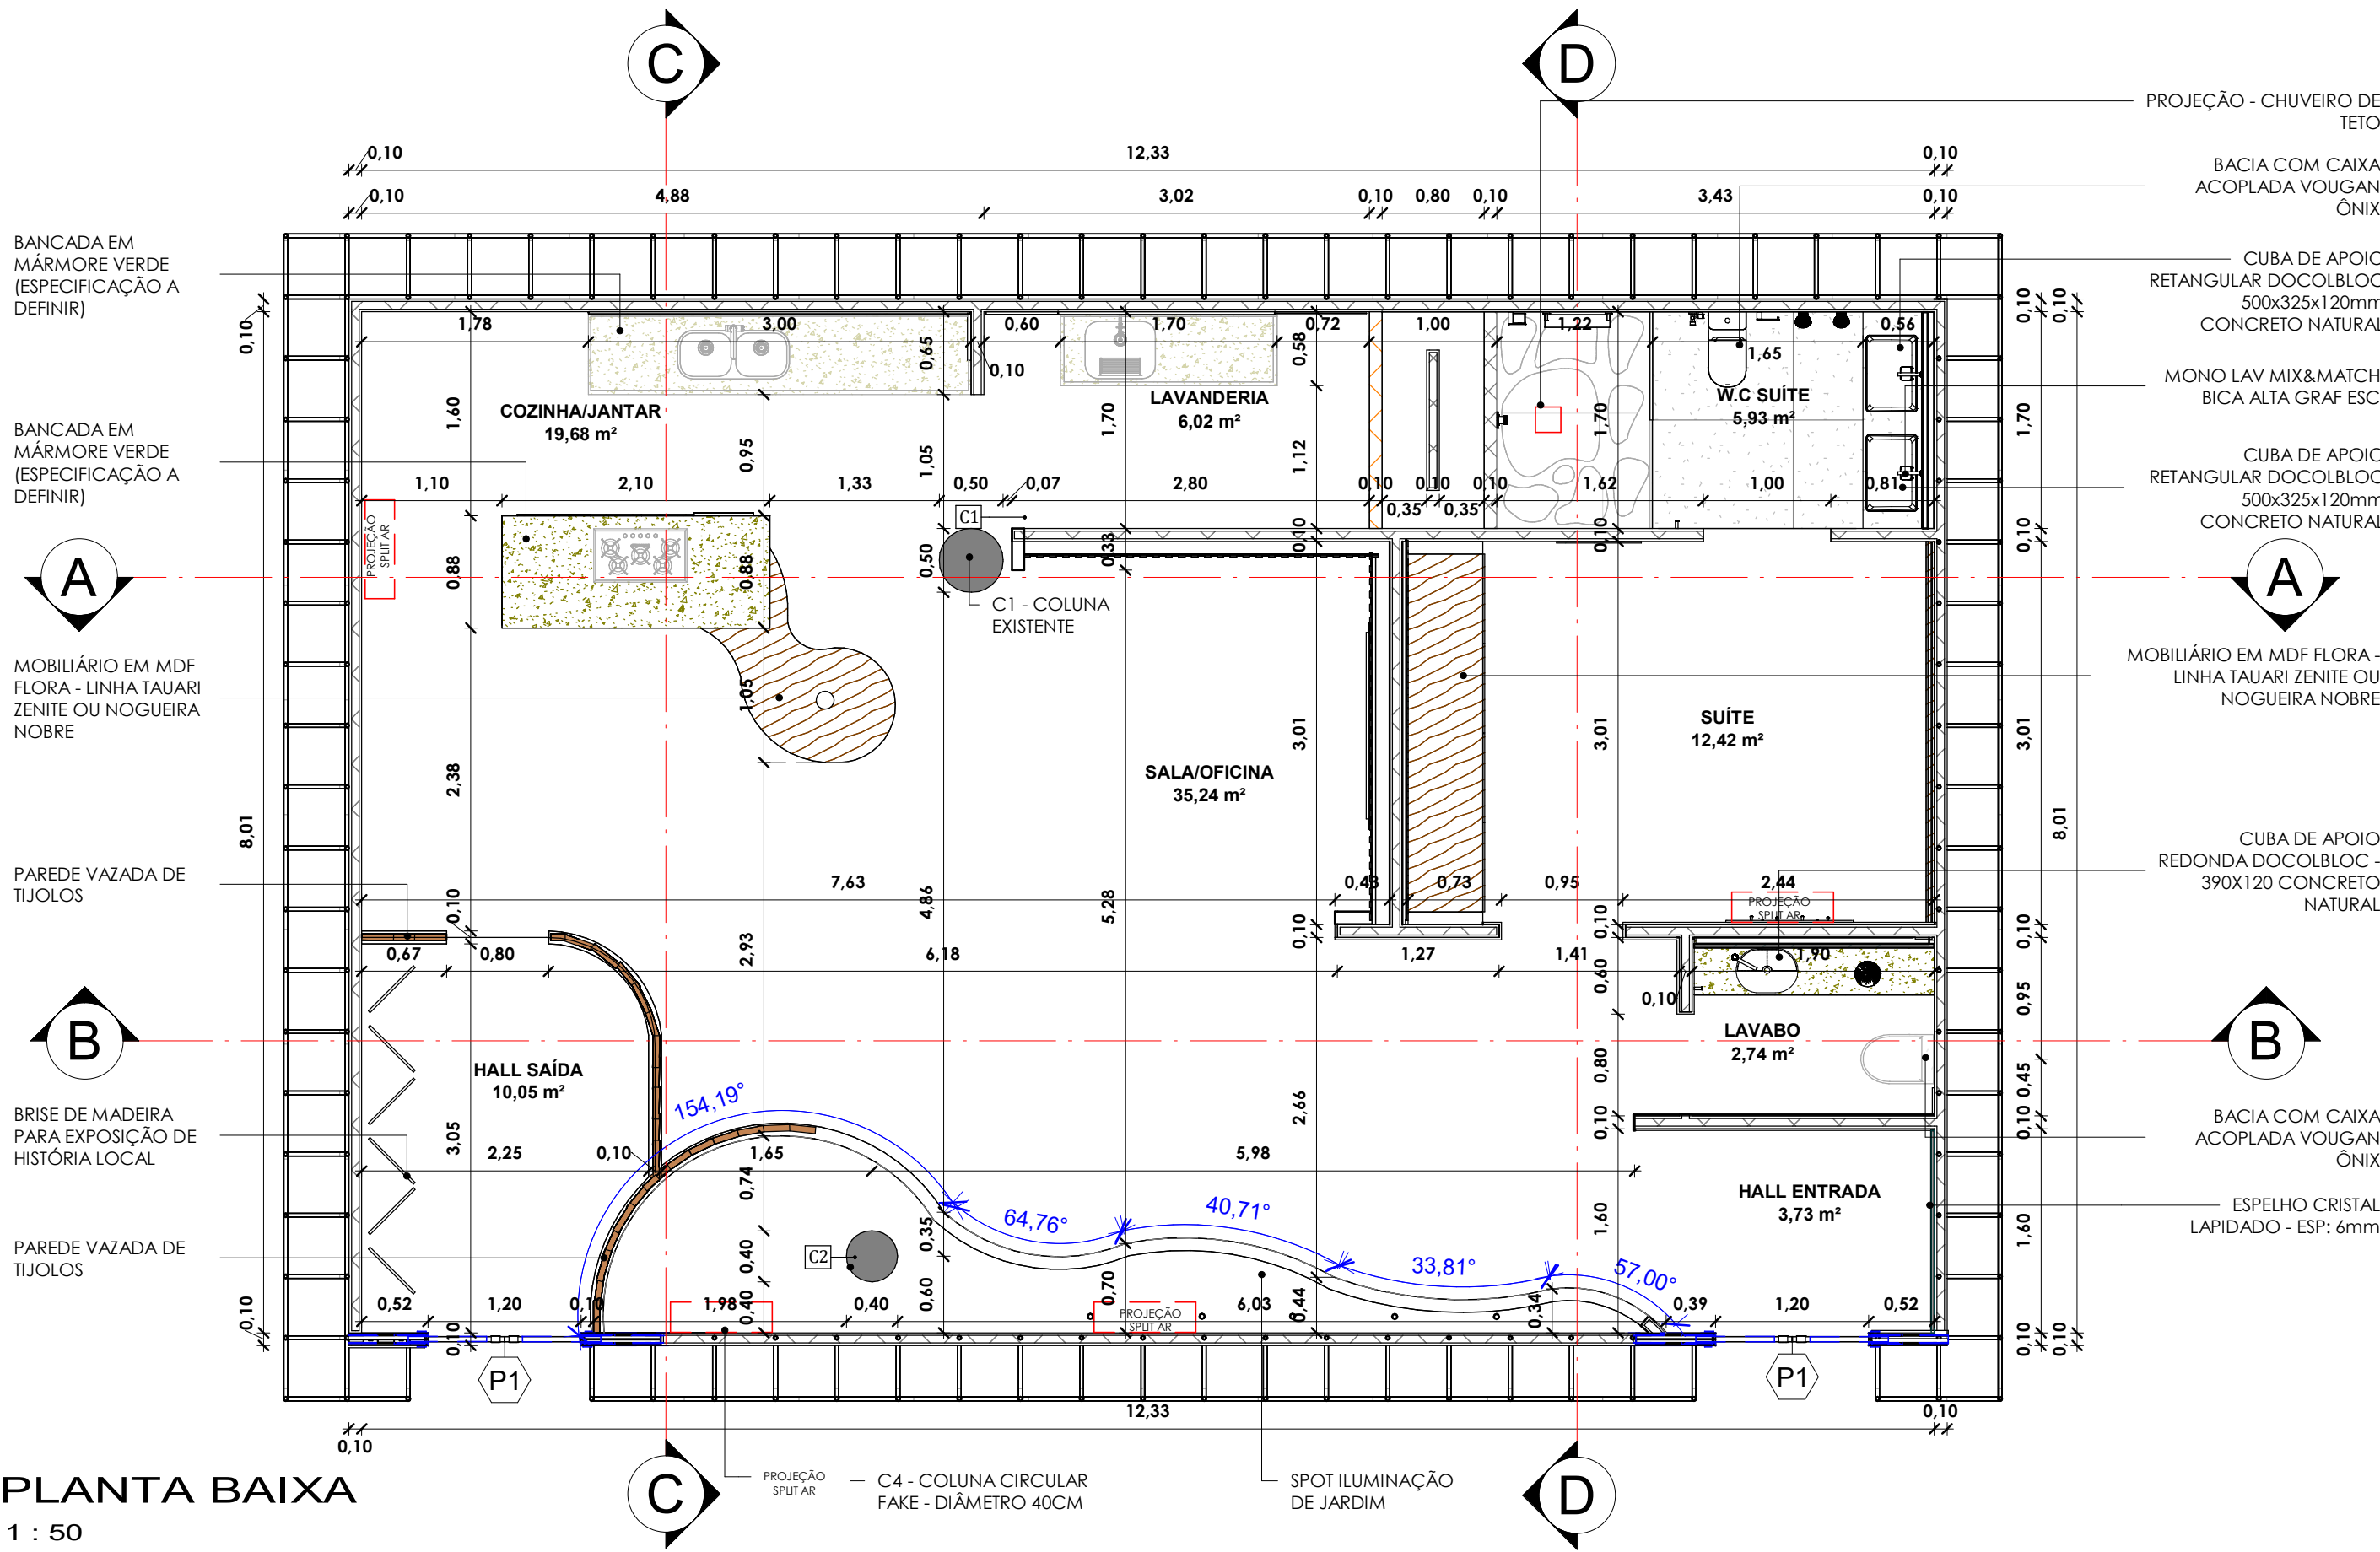

PLANTA BAIXA
1 : 50

QUADRO - ÁREA ÚTIL	
NOME	ÁREA
PLANTA BAIXA	
COZINHA/JANTAR	19,68 m²
HALL ENTRADA	3,73 m²
HALL SAÍDA	10,05 m²
LAVABO	2,74 m²
LAVANDERIA	6,02 m²
SALA/OFICINA	35,24 m²
SUÍTE	12,42 m²
W.C SUÍTE	5,93 m²
ÁREA ÚTIL TOTAL	95,82 m²

TABELA DE ESQUADRIAS - PORTAS				
NOME	DESCRIÇÃO	BASE	ALTURA	QUANT.
P1	PORTA DE CORRER EM MDF - 02 FOLHAS	1,20	2,50	2

LEGENDA GRÁFICA	
SÍMBOLO	DESCRIÇÃO
	PAREDE DE DRYWALL - ESP: 10CM
	PORCELANATO DANSK CEMENT WHITE
	PISO CIMENTÍCIO EXISTENTE

LEGENDA PILARES	
TIPO	DESCRIÇÃO
PILAR C1	PILAR EXISTENTE - DIÂMETRO 40 CM
PILAR C2	PILAR FALSO - DIÂMETRO 40 CM

IMPLEMENTAÇÃO DE EVENTO TEMPORÁRIO		Folha A01/30
Evento: Bienal de Arquitetura Brasileira - Pavilhão Roraima Local/Endereço: Av. Pedro Álvares Cabral, s/n - Vila Mariana, São Paulo - SP, 04094-050 Data/Horário: 25 de março a 30 de abril de 2026 - das 12h às 21h Responsável pelo Evento: SOLAR DAS ARTES – Instituto de Cultura e Integração de Arquitetura e Design CPF/CNPJ: 04.582.857/0001-18 Contribuinte: 036.144.0003-4 Escala: Como indicada		
Situação s/escala	Declaro que a aceitação deste projeto não implica no reconhecimento por parte da PMSP do direito de aprovação, execução de obras permanentes. O local será utilizado em período restrito de tempo ou com prazo determinado de duração e todas as montagens para realização de evento / instalações temporárias serão retiradas após o término do mesmo. Declaro ter conhecimento que o presente projeto refere-se à análise do evento / instalação temporária focada exclusivamente na salvaguarda dos bens protegidos, devendo ser observadas pelo proponente as demais legislações pertinentes, bem como as respectivas aprovações em outros órgãos públicos. Declaro ser responsável por garantir a integridade dos bens tombados ficando responsável por reparar eventuais danos; Esta planta é fiel ao evento proposto.	
Áreas Úteis (m²) Hall Entrada: 19,68 m² / Sala/Oficina: 35,24 m² Lavabo: 2,74 m² / Cozinha/Jantar: 19,68 m² Lavanderia: 6,02 m² / Suíte: 12,42 m² W.C Suíte: 5,93 m² / Hall Saída: 10,05 m² Área Construída Total: 100 m²	Responsável pelo Evento: SOLAR DAS ARTES Instituto de Cultura e Integração de Arquitetura e Design CNPJ: 04.582.857/0001-18 Responsável Técnico Projeto: Nome: NATASSIA DE AZEVEDO SOUZA CRUZ SILVA CAU: 000A434450 DEBORAH RODRIGUES FIOROTTI / CAU: A295921-6 DIEGO DE PAULA VASCONCELOS / CAU: A149911-4 ADRIANO ARAUJO LIMA GODINHO / CAU: 00A3153207 RAYRESSON LIMA DA ROCHA / CAU: 00A2755270	
Lotação Máxima: 100 pessoas	RRT: SI16505384I00CT001	