


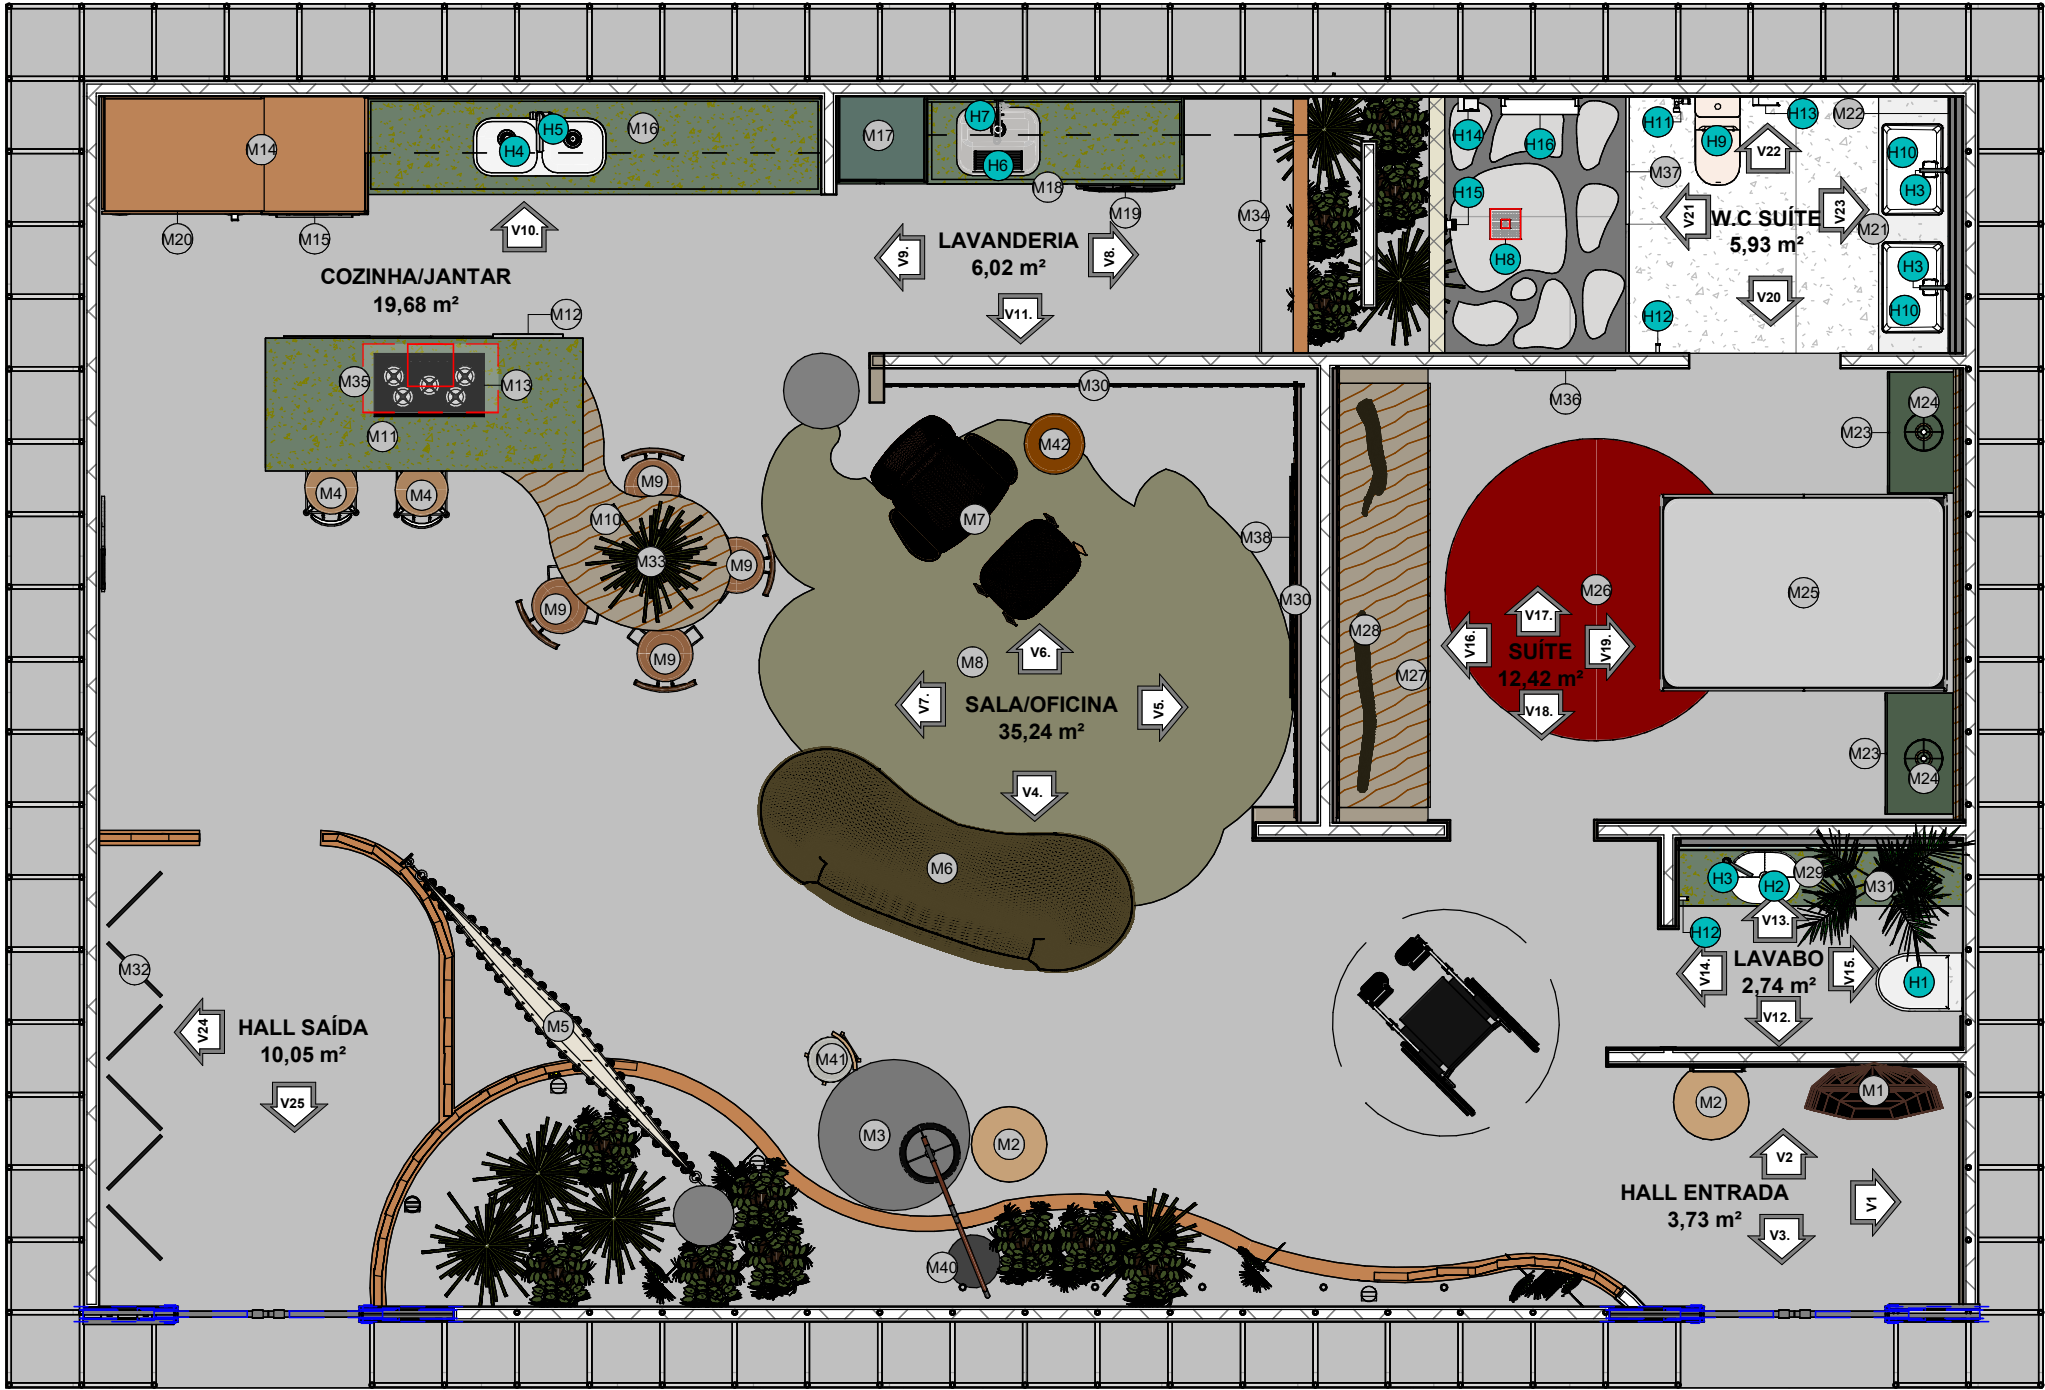

LAYOUT - RORAIMA

1 : 50

TABELA DE PEÇAS HIDROSSANITÁRIAS			
CÓD	DESCRIÇÃO	FORNEC.	QUANT.
H1	BACIA COM CAIXA ACOPLADA VOUGAN ÔNIX	DOCOL	1
H2	CUBA DE APOIO REDONDO DOCOLBLOC 390x120mm CONCRETO NATURAL	DOCOL	1
H3	MONO LAV MIX&MATCH BICA ALTA GRAF ESC	DOCOL	3
H4	Cuba Spice 83,5x34,5x18 CD0 alto brilho c/vsa 4,5"	DOCOL	1
H5	MIST MONO COZ N DOCOLVITALIS GRF ESC	Docol	1
H6	TANQUE MONIBLOCO 50X40X23 ALTO BRILHO 32L	DOCOL	1
H7	TORNEIRA LONGA 1158 DE PAREDE LEED TRIOCROMADO	DOCOL	1
H8	CHUVEIRO DE TETO Q200 1/2 DOCOL HEAVEN GRAFITE ESCOVADO	DOCOL	1
H9	BACIA COM CAIXA ACOPLADA VOUGAN ÔNIX	DOCOL	1
H10	CUBA DE APOIO RETANGULAR BLOC 500x325x120mm CONCRETO NATURAL	DOCOL	2
H11	DUCHA HIGIÊNICA COM REGISTRO DE PAREDE PARA LAVATÓRIO MIX&MATCH GRAFITE ESCOVADO	DOCOL	1

TABELA DE PEÇAS HIDROSSANITÁRIAS			
CÓD	DESCRIÇÃO	FORNEC.	QUANT.
H12	CABIDE PROJ 466 CR - CROMADO	DOCOL	2
H13	PAPELEIRA PROJ 466 CR - CROMADO	DOCOL	1
H14	SABONETEIRA PROJ 466 CR - CROMADO	DOCOL	1
H15	ACABAMENTO MONOCOMANDO PARA CHUVEIRO ALTA VAZÃO 3/4 CROMADO	DOCOL	1
H16	PRATELEIRA ACRILICA CROMADA SQUARE	DOCOL	1

TABELA DE MOBILIÁRIO1			
CÓD	DESCRIÇÃO	FORNECEDOR	QUANT.
M1	ARMÁRIO CANOA	ARTISTA LOCAL	1
M2	MESA LATERAL REDONDA DE MADEIRA	FORNECEDOR A DEFINIR	2
M3	MESA ORGÂNICA TAUPE	WESTWING	1
M4	BANQUETA TROPICÁLIA EM CORDA NÁUTICA - CINZA E COBRE	WESTWING	2
M5	REDE DE FIBRA	FORNECEDOR LOCAL	1
M6	SOFÁ CURVO	LIDER	1
M7	POLTRONA E BANCO GUARUÇA	LIDER	1
M8	TAPETE CAJU	TAPETAH	1
M9	CADEIRA OKO	SACCARO	4
M10	TAMPO DE MESA EM MDF FLORA - LINHA TAUARI ZENETI	FLORA	1
M11	BANCADA EM MÁRMORE VERDE (A DEFINIR ESPECIFICAÇÃO)	FORNECEDOR A DEFINIR	1
M12	LAVA LOUÇAS LS10E	ELECTROLUX	1
M13	COOKTOP KE5GW	ELECTROLUX	1
M14	ARMARIO EM MDF FLORA - LINHA SOLAR SUPERMATT	FLORA	1
M15	TORRE QUENTE OE8EW E ME3BC	ELECTROLUX	1
M16	BANCADA EM MÁRMORE VERDE (A DEFINIR ESPECIFICAÇÃO)	FORNECEDOR A DEFINIR	1
M17	ARMÁRIO EM MDF FLORA - LINHA FLORESTA SUPERMATT	FLORA	1
M18	BANCADA EM MÁRMORE VERDE (A DEFINIR ESPECIFICAÇÃO)	FORNECEDOR A DEFINIR	1
M19	LAVA E SECA VC4	ELECTROLUX	1
M20	GELADEIRA MODELO IM8S	ELECTROLUX	1
M21	BANCADA EM MÁRMORE BRANCO (A DEFINIR ESPECIFICAÇÃO)	FORNECEDOR A DEFINIR	1
M22	PAINEL COM ESPELHO RETROILUMINADO	FORNECEDOR A DEFINIR	1
M23	MESA DE CABECEIRA ONDULADA MAXI VERDE	WESTWING	2
M24	ABAJUR GARABE NATURAL	WESTWING	2
M25	CAMA DE CASAL - ESTRADO LUX	LIDER	1
M26	TAPETE BURITI (RORAIMA)	TAPETAH	1
M27	MOBILIÁRIO EM MDF FLORA - LINHA TAUARI ZENITE OU NOGUEIRA NOBRE	FLORA	1
M28	CABIDE EM GALHO DE ÁRVORE ORGÂNICO	FORNECEDOR A DEFINIR	1
M29	BANCADA EM MÁRMORE VERDE (A DEFINIR ESPECIFICAÇÃO)	FORNECEDOR A DEFINIR	1
M30	PAINEL MUXARABI COM TELA TENSIONADA ILUMINADA	FORNECEDOR A DEFINIR	2
M31	PÉ DE BURITI ARTIFICIAL	ARTISTA LOCAL	1
M32	PAINEL EXPOSITOR EM MADEIRA	FORNECEDOR A DEFINIR	1
M33	VASO COM PÉ DE MURICI - VER DET.	FORNECEDOR A DEFINIR	1
M34	VARAL RETRÁTIL EM AÇO INOX	DECA	1
M35	COIFA CE9TF	ELECTROLUX	1
M36	ESPELHO FORMATO ORGÂNICO	FORNECEDOR A DEFINIR	1
M37	BOX DE VIDRO TEMPERADO LINEAR	FORNECEDOR A DEFINIR	1
M38	TELEVISÃO 65 POLEGADAS	TCL	1
M39	CABIDEIRO PONTO	LIDER	1
M40	LUMINÁRIA ARTESANAL BURITI	FORNECEDOR A DEFINIR	1
M41	BANQUETA MARINA	LIDER	1
M42	MESA LATERAL REDONDA BRILHO VERMELHA	WESTWING	1

BAB - BIENAL DA ARQUITETURA BRASILEIRA - RORAIMA

Folha
A02/30

Evento: Bienal de Arquitetura Brasileira - Pavilhão Roraima

Local/Endereço: Av. Pedro Álvares Cabral, s/n - Vila Mariana, São Paulo - SP, 04094-050

Data/Horário: 25 de março a 30 de abril de 2026 - das 12h às 21h

Responsável pelo Evento: SOLAR DAS ARTES
– Instituto de Cultura e Integração de Arquitetura e Design

CPF/CNPJ: 04.582.857/0001-18

Contribuinte: 036.144.0003-4

Escala: 1 : 50

Situação s/escala	Declaro que a aceitação deste projeto não implica no reconhecimento por parte da PMSP do direito de aprovação, execução de obras permanentes. O local será utilizado em período restrito de tempo ou com prazo determinado de duração e todas as montagens para realização de evento / instalações temporárias serão retiradas após o término do mesmo. Declaro ter conhecimento que o presente projeto refere-se à análise do evento / instalação temporária focada exclusivamente na salvaguarda dos bens protegidos, devendo ser observadas pelo proponente as demais legislações pertinentes, bem como as respectivas aprovações em outros órgãos públicos. Declaro ser responsável por garantir a integridade dos bens tombados ficando responsável por reparar eventuais danos; Esta planta é fiel ao evento proposto.
Áreas Úteis (m²) Hall Entrada: 19,68 m² / Sala/Oficina: 35,24 m² Lavabo: 2,74 m² / Cozinha/Jantar: 19,68 m² Lavanderia: 6,02 m² / Suite: 12,42 m² W.C Suite: 5,93 m² / Hall Saída: 10,05 m² Área Construída Total: 100 m²	Responsável pelo Evento: SOLAR DAS ARTES Instituto de Cultura e Integração de Arquitetura e Design CNPJ: 04.582.857/0001-18 Responsável Técnico Projeto: Nome: NATASSIA DE AZEVEDO SOUZA CRUZ SILVA CAU: 000A434450 DEBORAH RODRIGUES FIOROTTI / CAU: A295921-6 DIEGO DE PAULA VASCONCELOS / CAU: A149911-4 ADRIANO ARAUJO LIMA GODINHO / CAU:00A3153207 RAYRESSON LIMA DA ROCHA / CAU: 00A2755270
Lotação Máxima: 100 pessoas	RRT: SI16505384I00CT001